


План 1-го этажа


Экспликация помещений

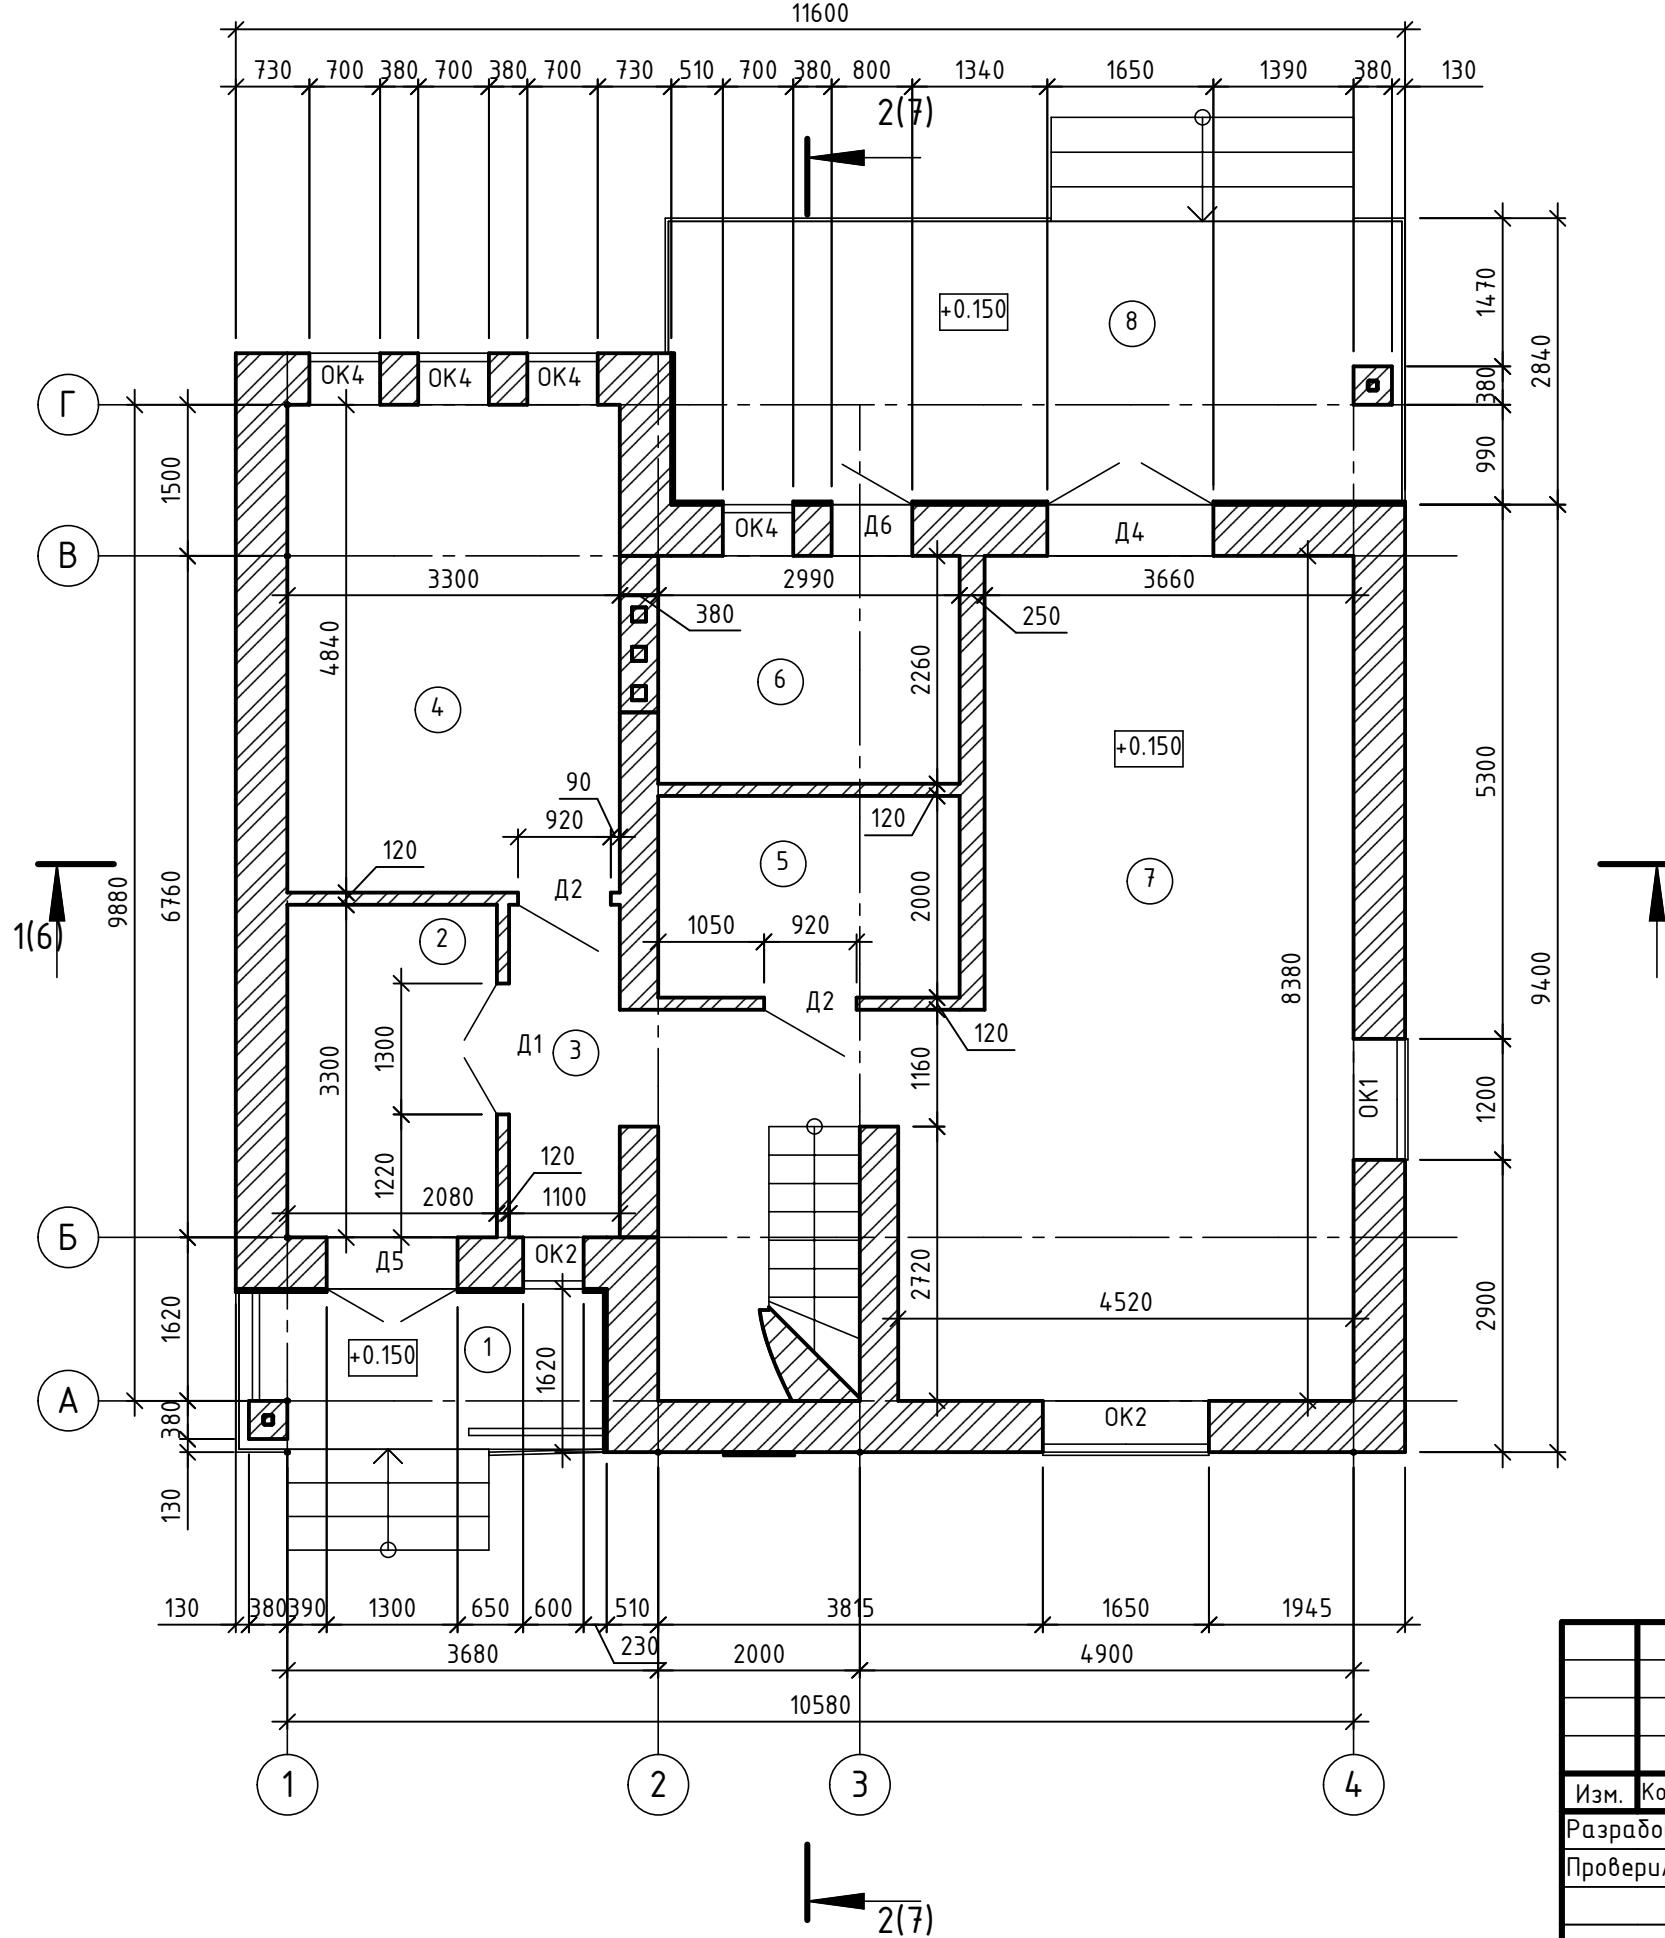

Номер помещения	Наименование	Площадь, м ²	Кат. помещений
1	Крыльцо	5.96	
2	Тамбур	6.86	
3	Холл с лестничной клеткой	11.83	
4	Гостевая	15.97	
5	Санузел	5.98	
6	Бойлерная	6.76	
7	Кухня-столовая	34.01	
8	Терраса	20.68	
	Итого:	108.05	


Экспликация помещений

План 2-го этажа

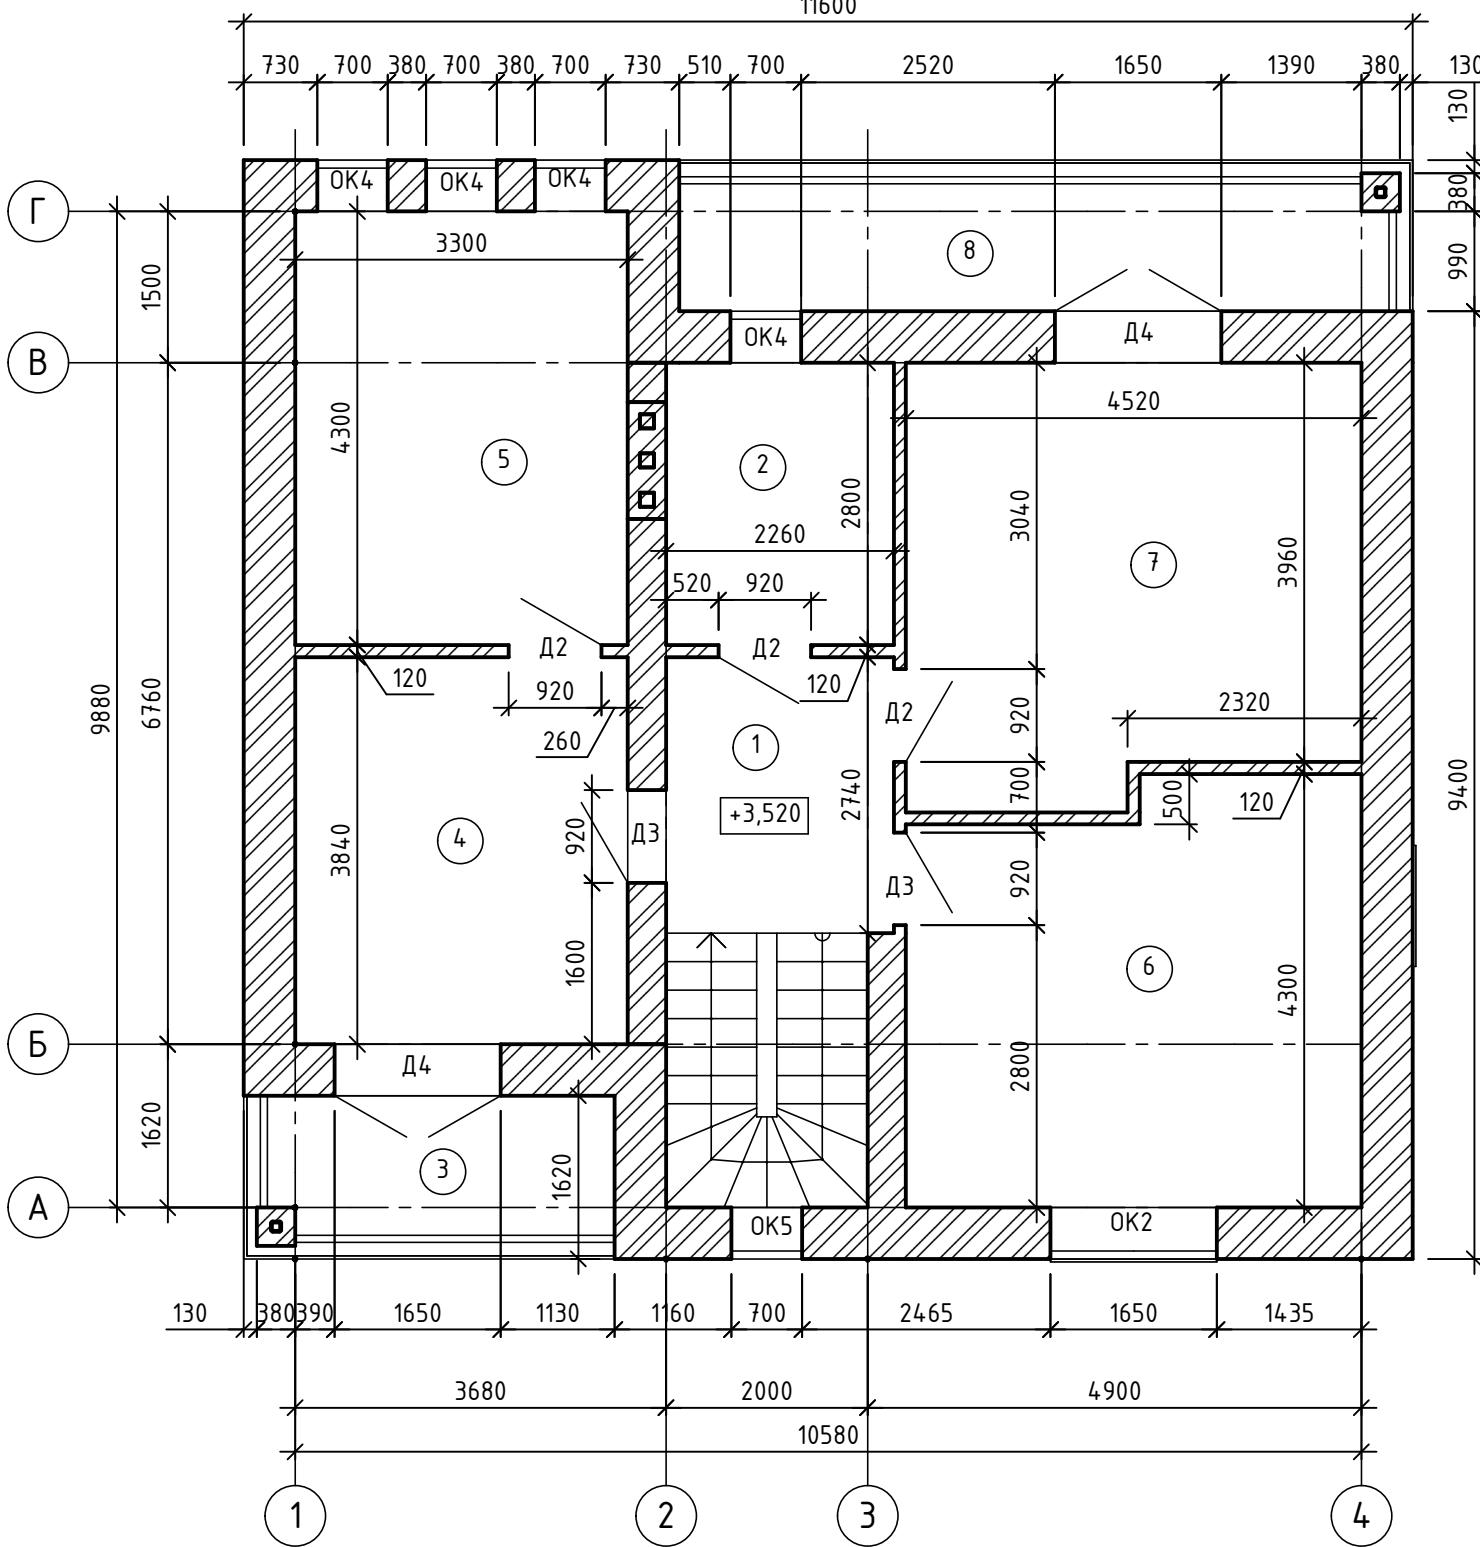

Номер помещения	Наименование	Площадь, м ²	Кат. помещений
1	Холл с лестничной клеткой	11.63	
2	Санузел	6.33	
3	Балкон	5.96	
4	Детская	12.67	
5	Спальня	14.19	
6	Спальня	18.28	
7	Спальня	19.00	
8	Балкон	10.92	
	Итого:	98.98	

Инф. № по док.	Подпись с датой	Взам. инф. №

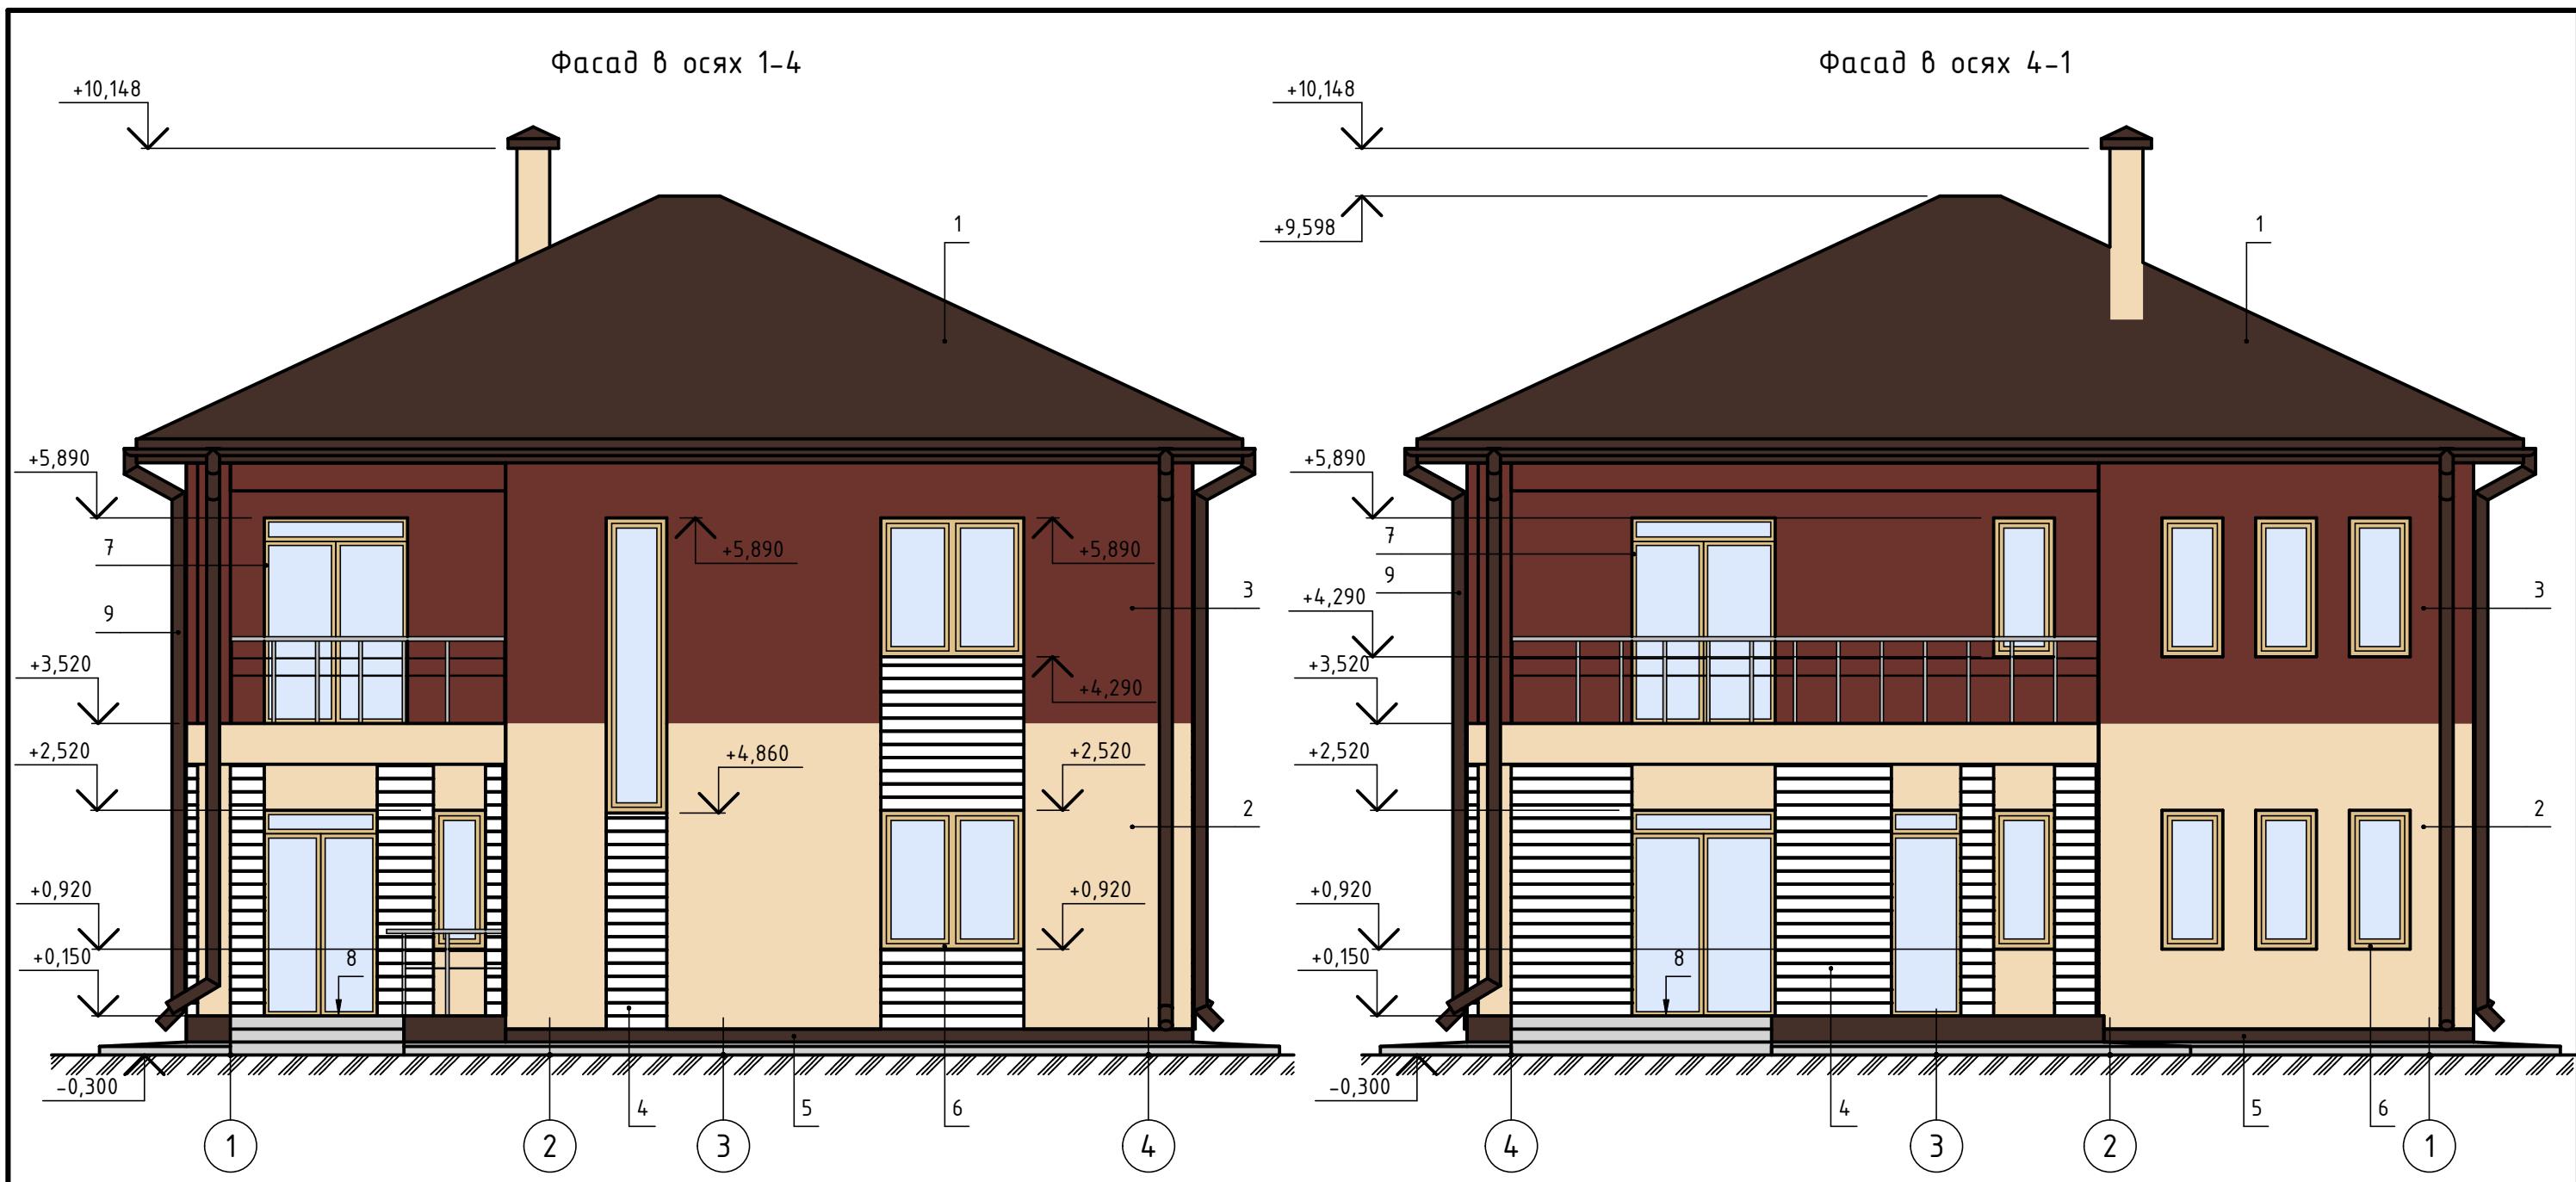


Ведомость отделки фасадов


Поз. отделки	Наименование элемента	Наименование материала отделки	Номер колера/ цвет	Эталон колера	Примечани
1	Кровля	Керамическая черепица	Шоколад		
2	Наружные стены	Штукатурка	Бежевый		
3	Наружные стены	Штукатурка	Красно-корич.		
4	Наружные стены	Доски	Белый		
5	Цоколь	Декоративный камень	Шоколад		
6	Окна	ПВХ	Янтарный		
7	Двери	ПВХ	Янтарный		
8	Крыльцо, терраса	Тротуарная плитка	Серый		
9	Водосточная система	Металл	Шоколад		

						АР
						Индивидуальный жилой дом
Изм.	Кол.уч	Лист	№док	Подпись	Дата	
Разработ.						Стадия
Проверил					Компетаж	Лист
						Листов
Н.контр.					Фасады в осях 1-4, 4-1	

Фасад в осях А-Г

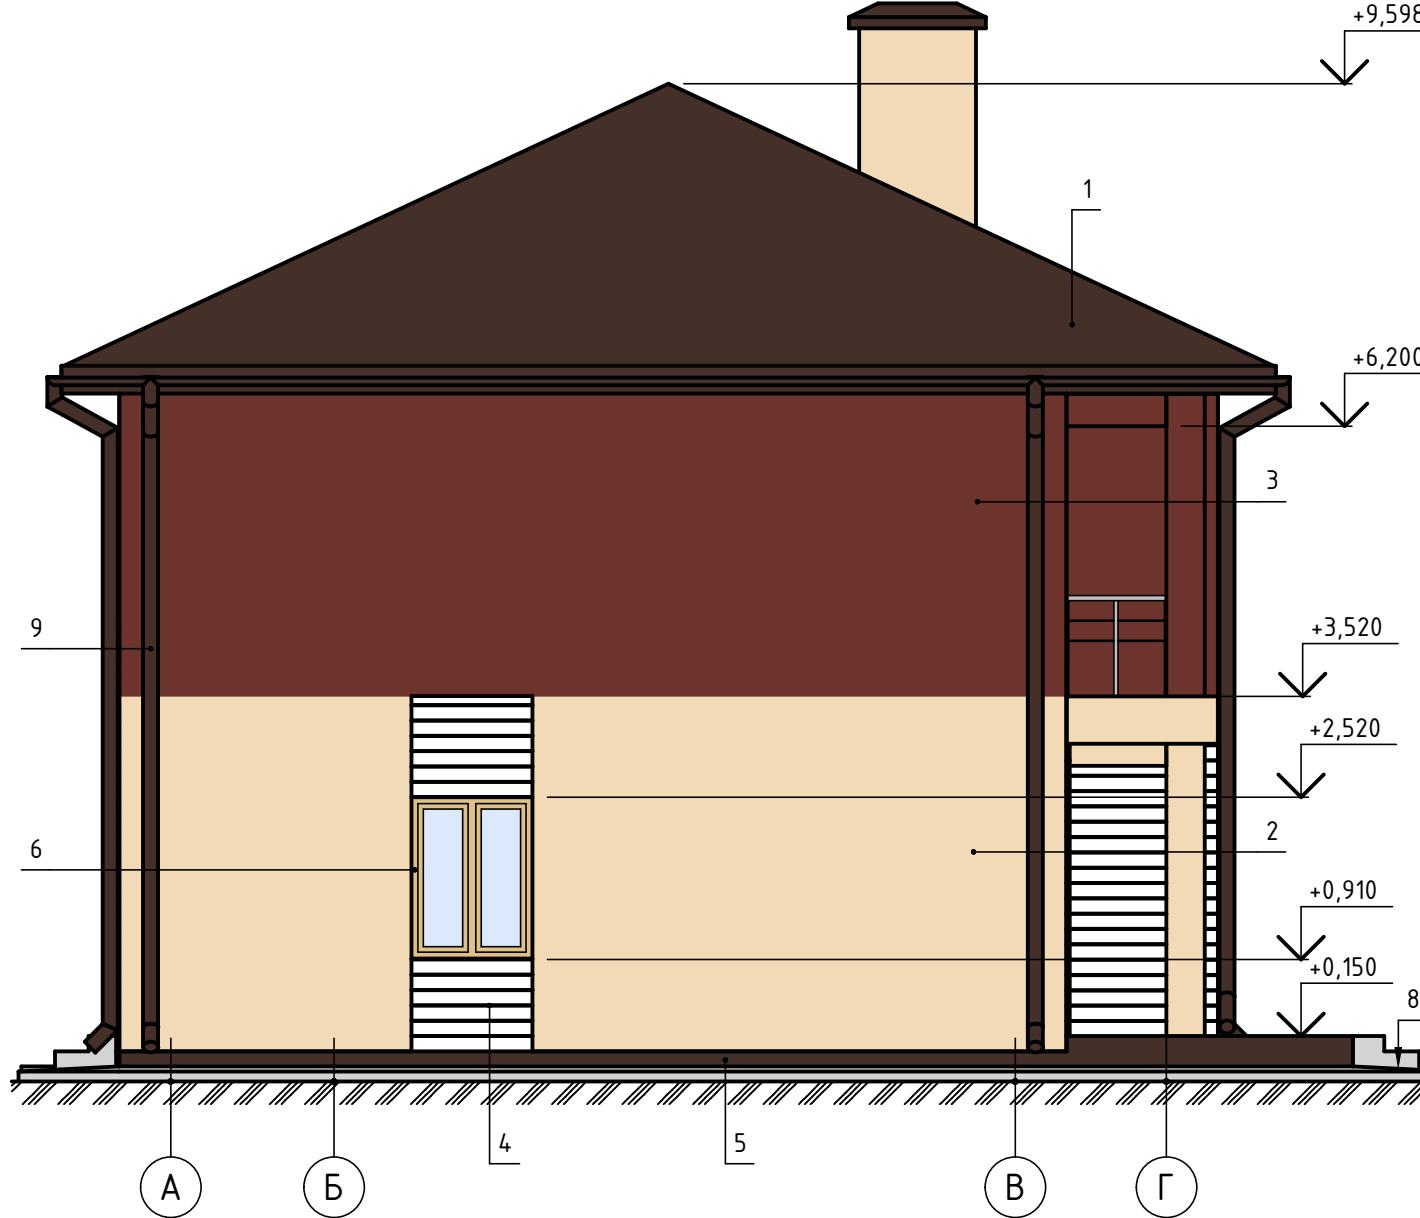

Фасад в осях Г-А

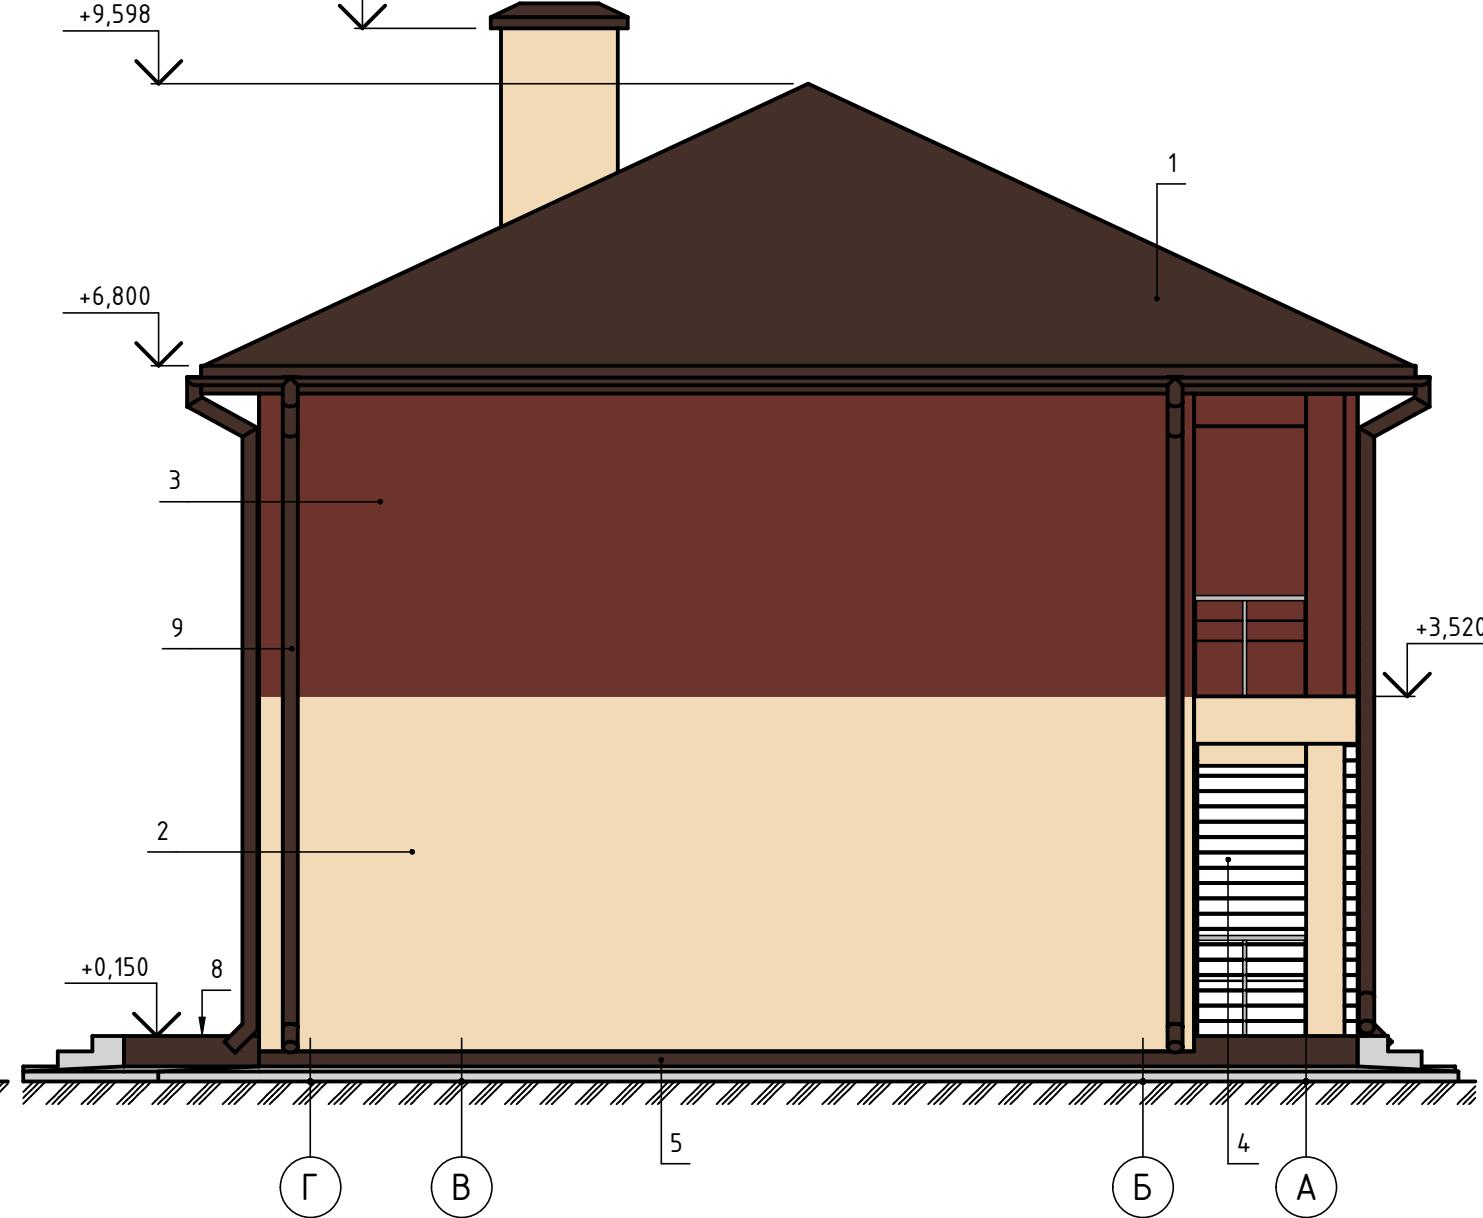

Ведомость отделки фасадов


Поз. №	Наименование элемента	Наименование материала отделки	Номер колера/ цвет	Эталон колера	Примечание
1	Кровля	Керамическая черепица	Шоколад		
2	Наружные стены	Штукатурка	Бежевый		
3	Наружные стены	Штукатурка	Красно-корич.		
4	Наружные стены	Доски	Белый		
5	Цоколь	Декоративный камень	Шоколад		
6	Окна	ПВХ	Янтарный		
7	Двери	ПВХ	Янтарный		
8	Крыльцо, терраса	Тротуарная плитка	Серый		
9	Водосточная система	Металл	Шоколад		


АР

Индивидуальный жилой дом

Изм.	Кол.уч	Лист	№док	Подпись	Дата	Стадия	Лист	Листов
Разработ.								
Проверил								
Н.контр.								


Компания
Фасады в осях А-Г, Г-А

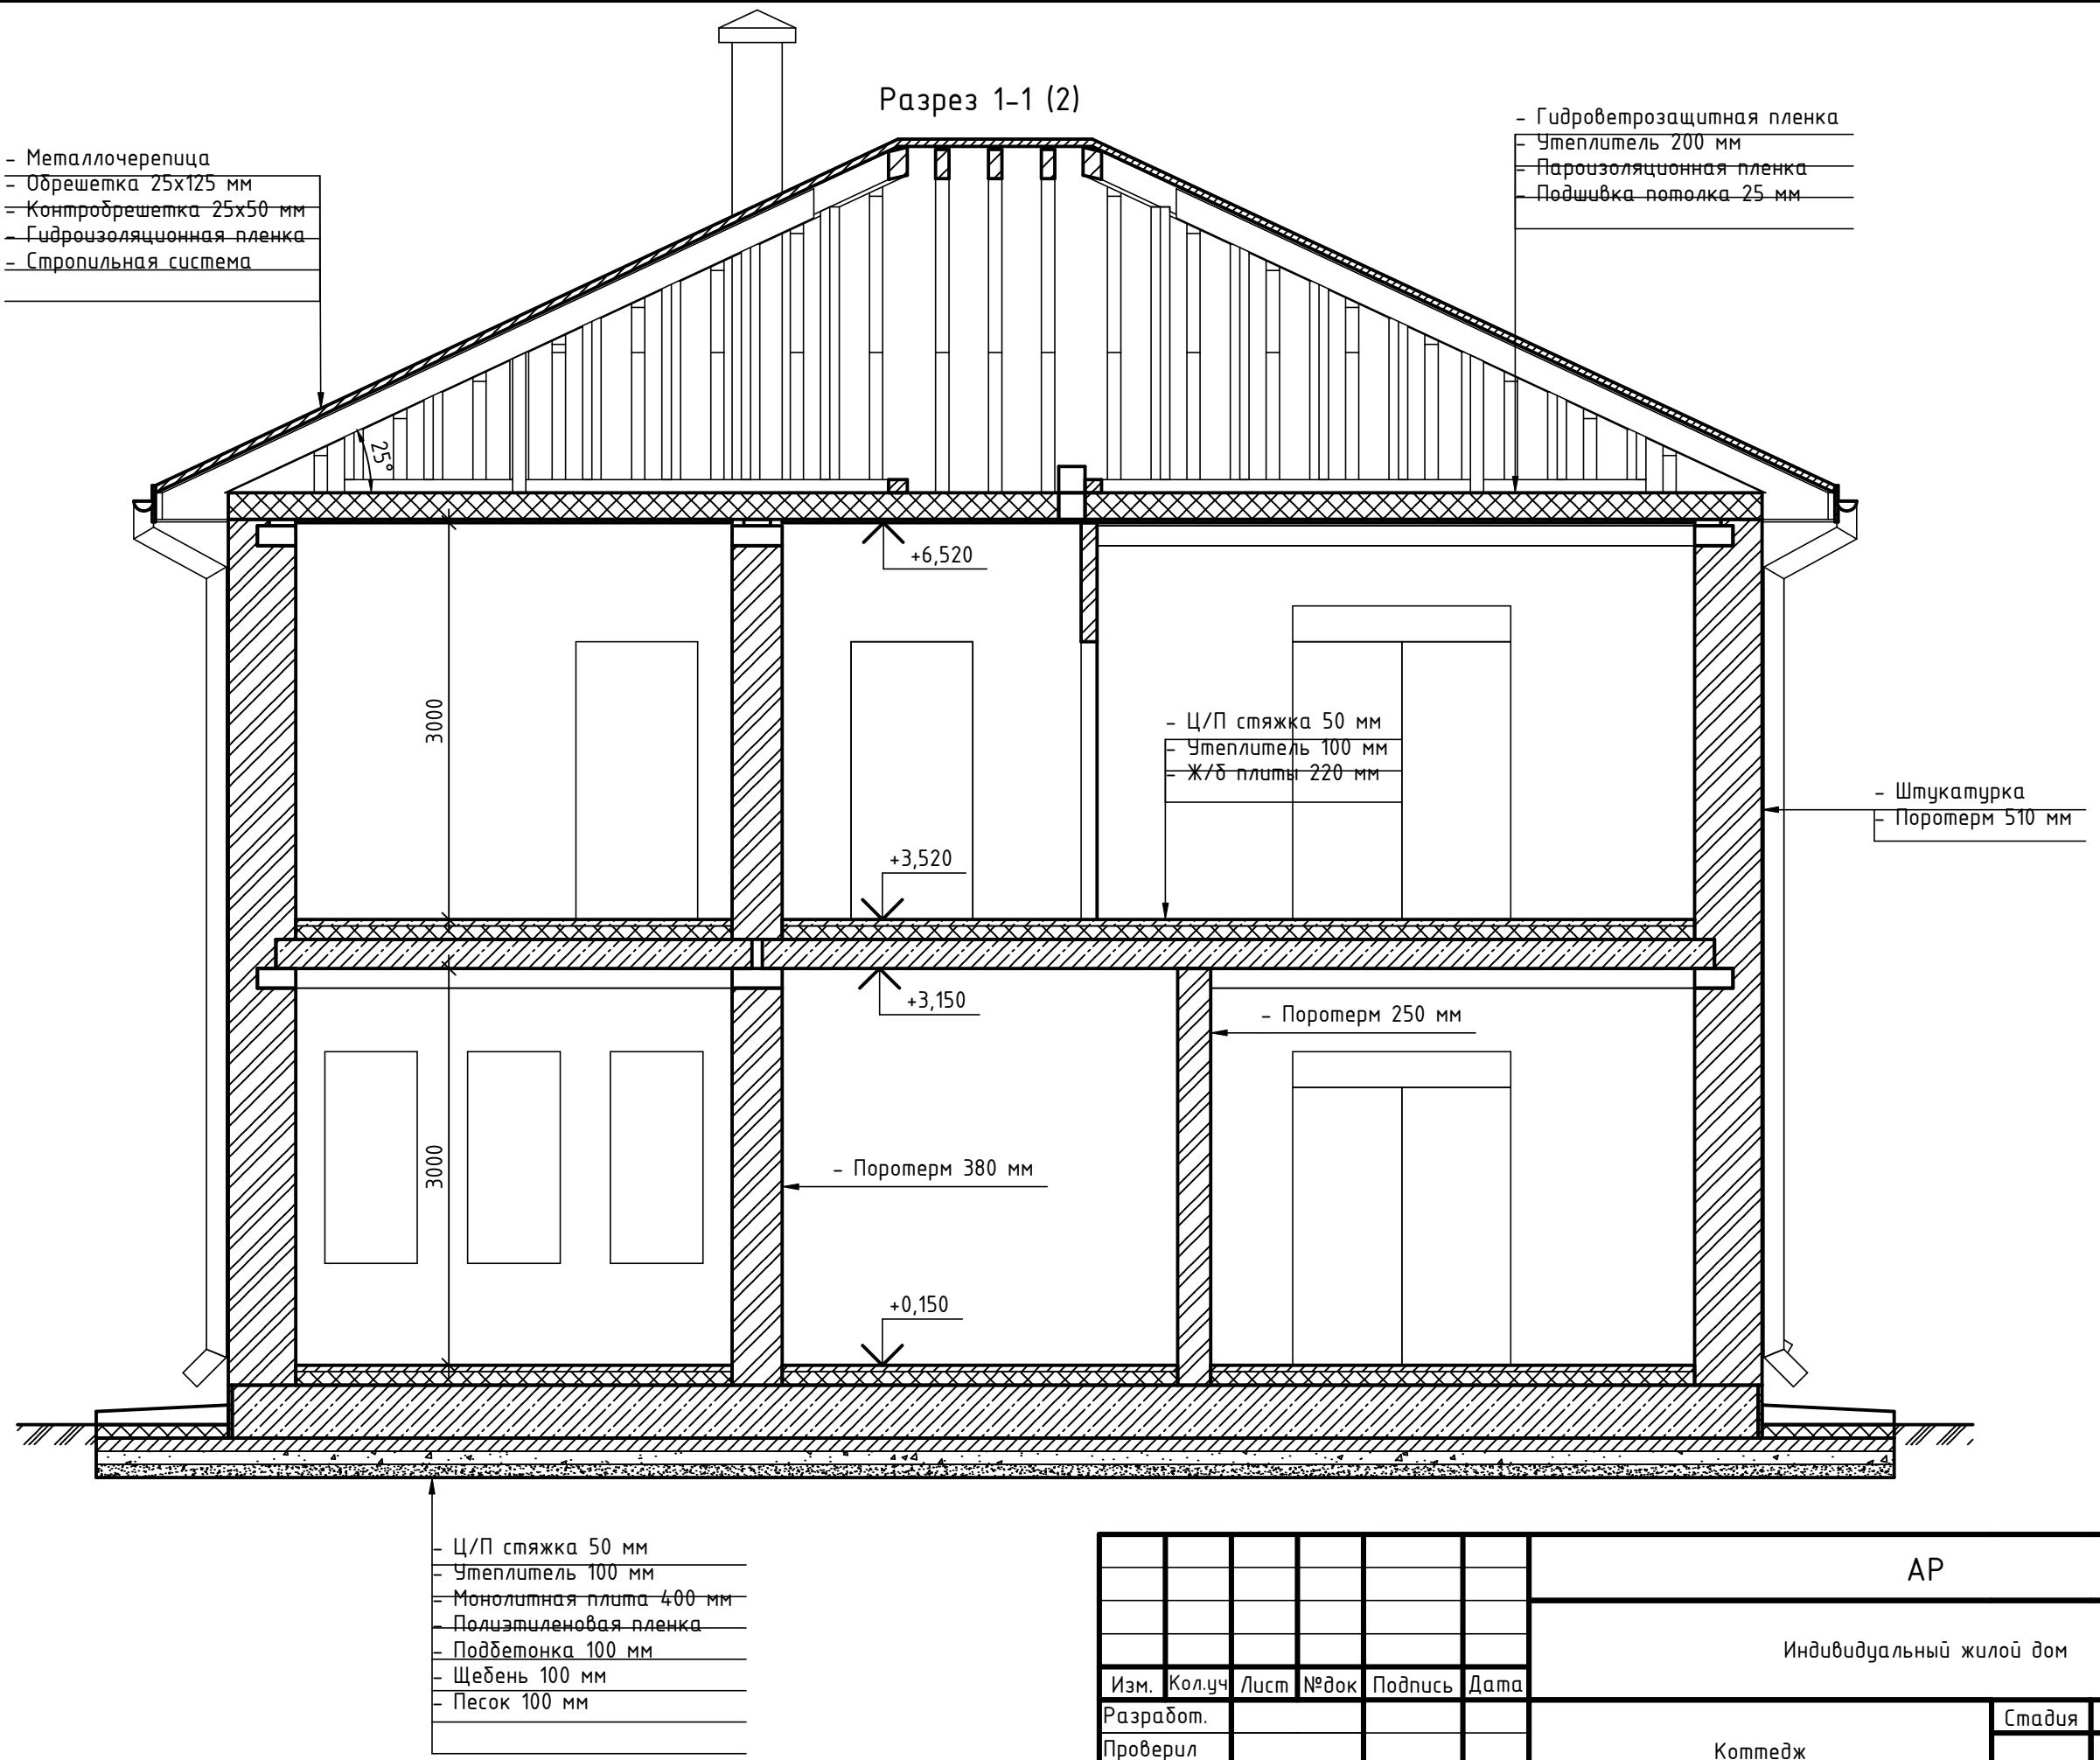

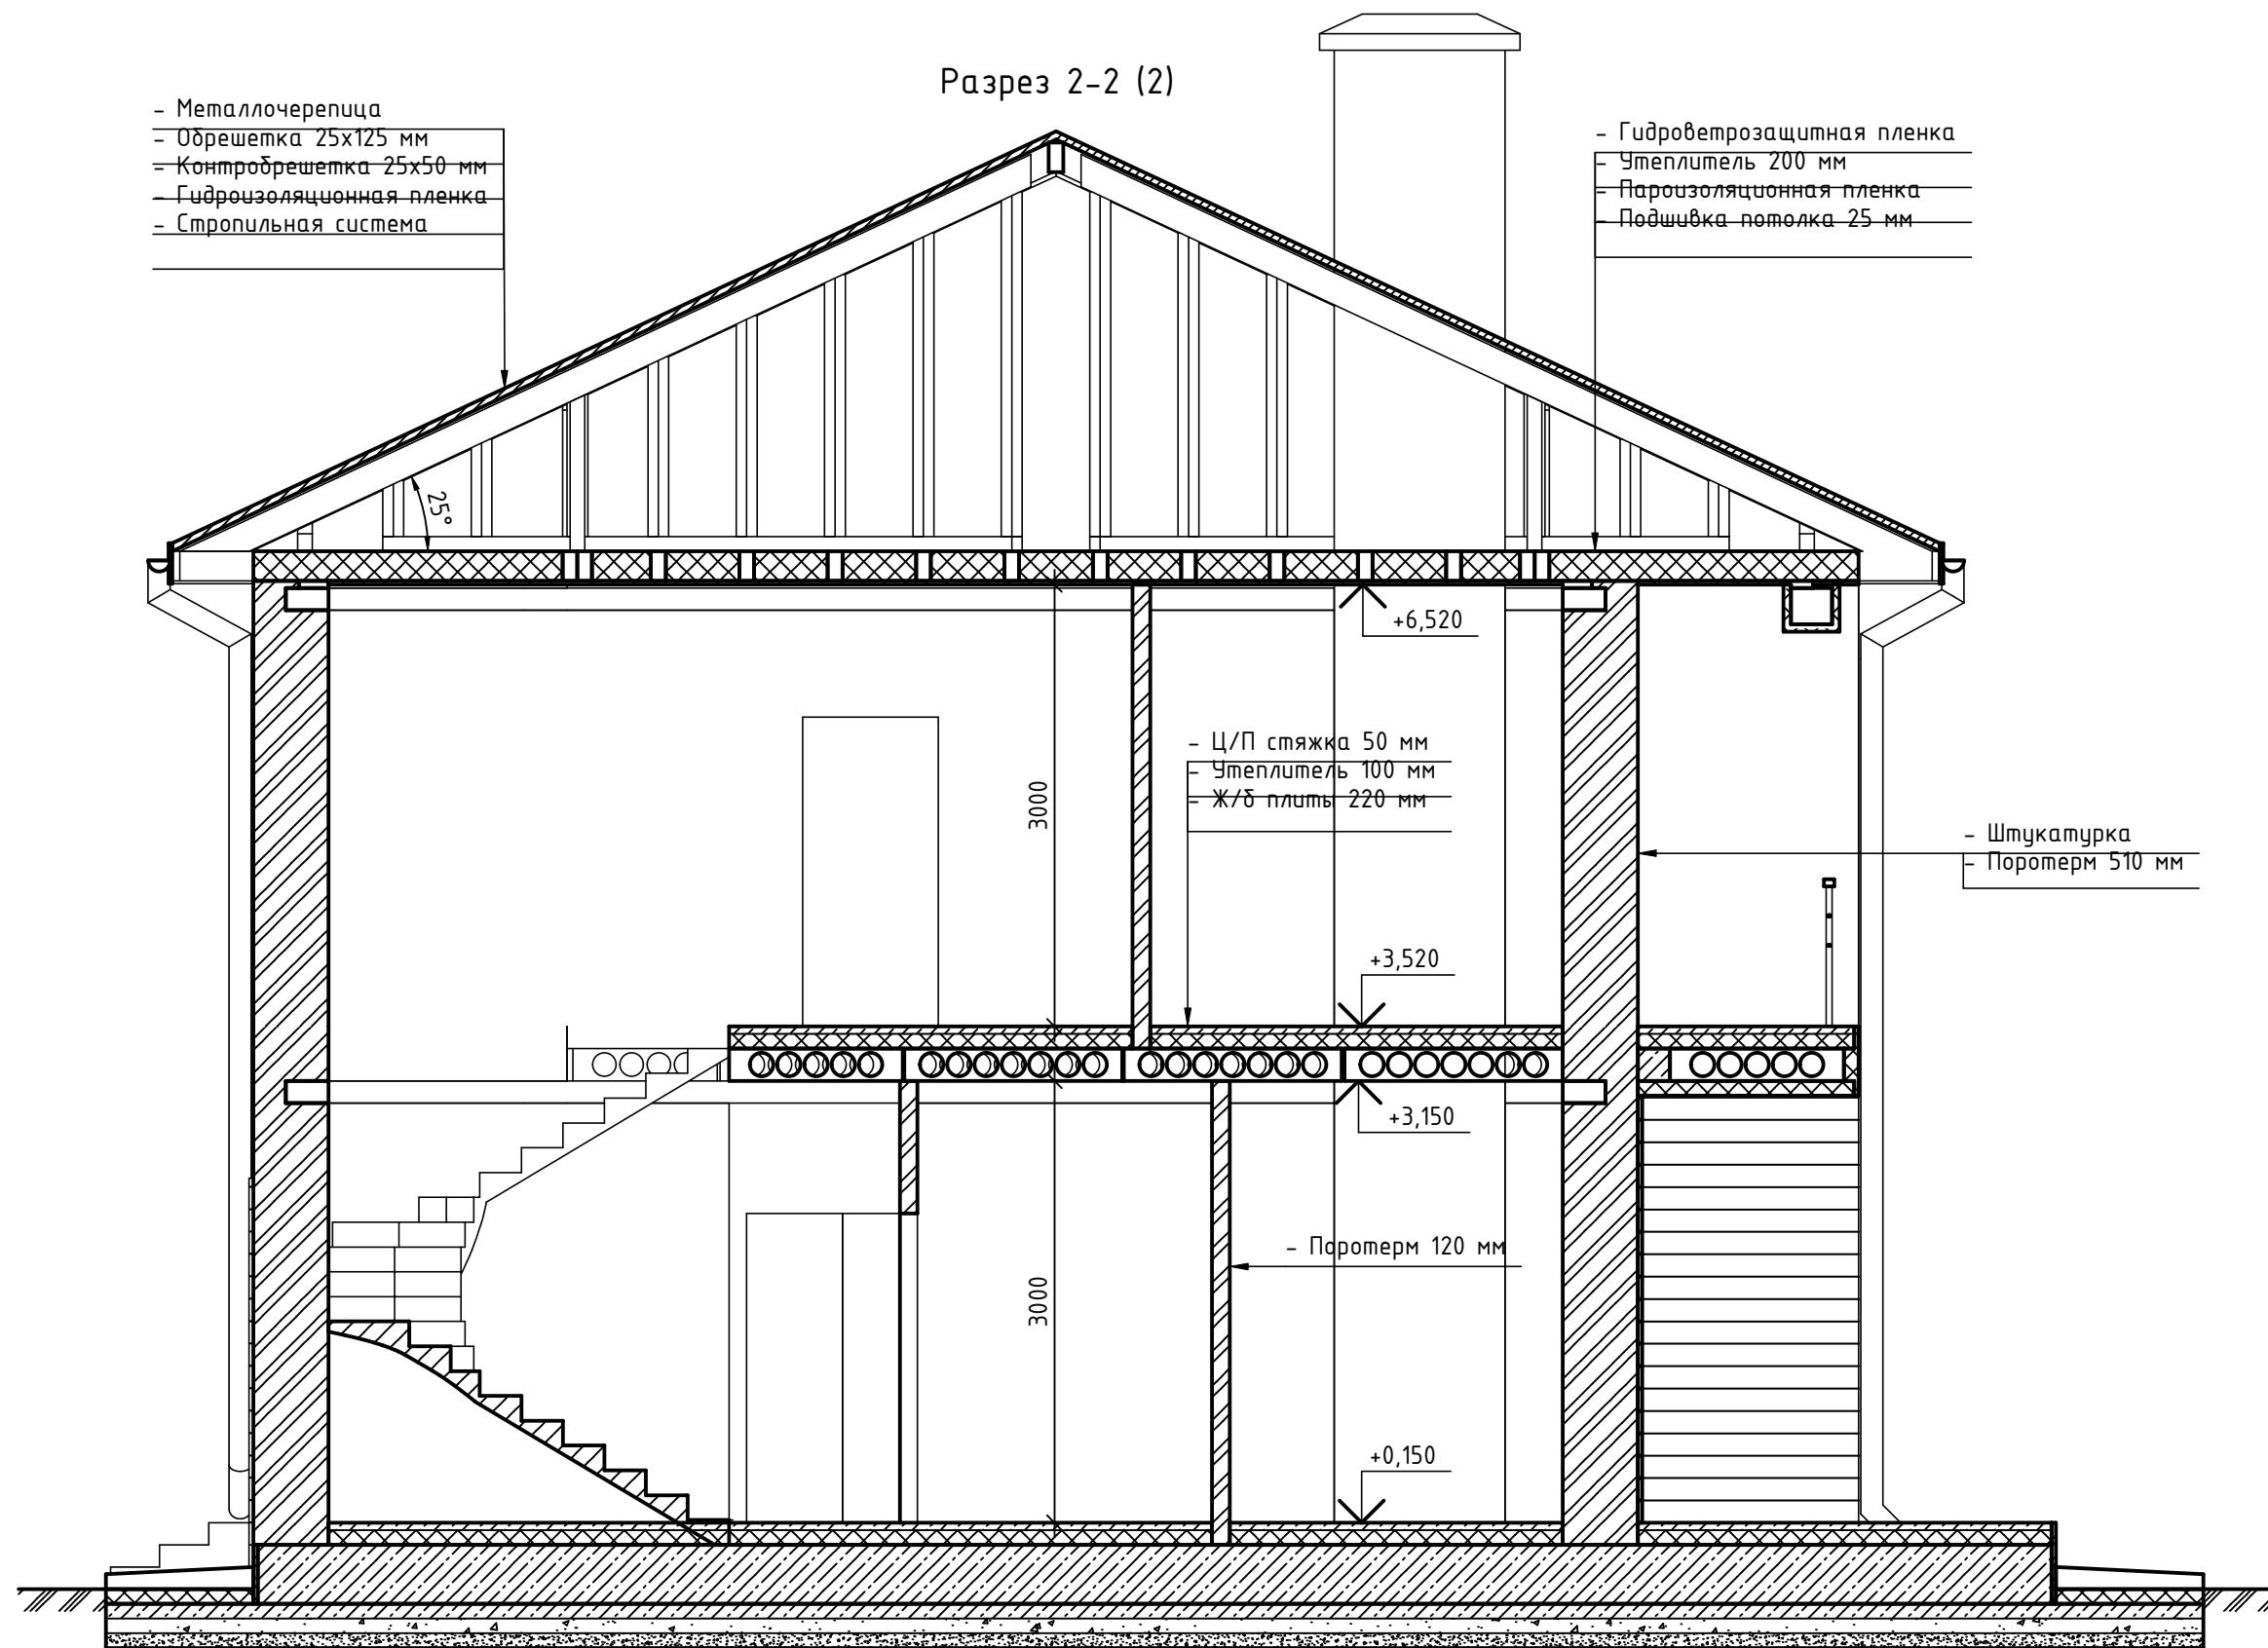


- Ц/П стяжка 50 мм
- Утеплитель 100 мм
- Монолитная плита 400 мм
- Полиизтиленовая пленка
- Подбетонка 100 мм
- Щебень 100 мм
- Песок 100 мм

План кровли

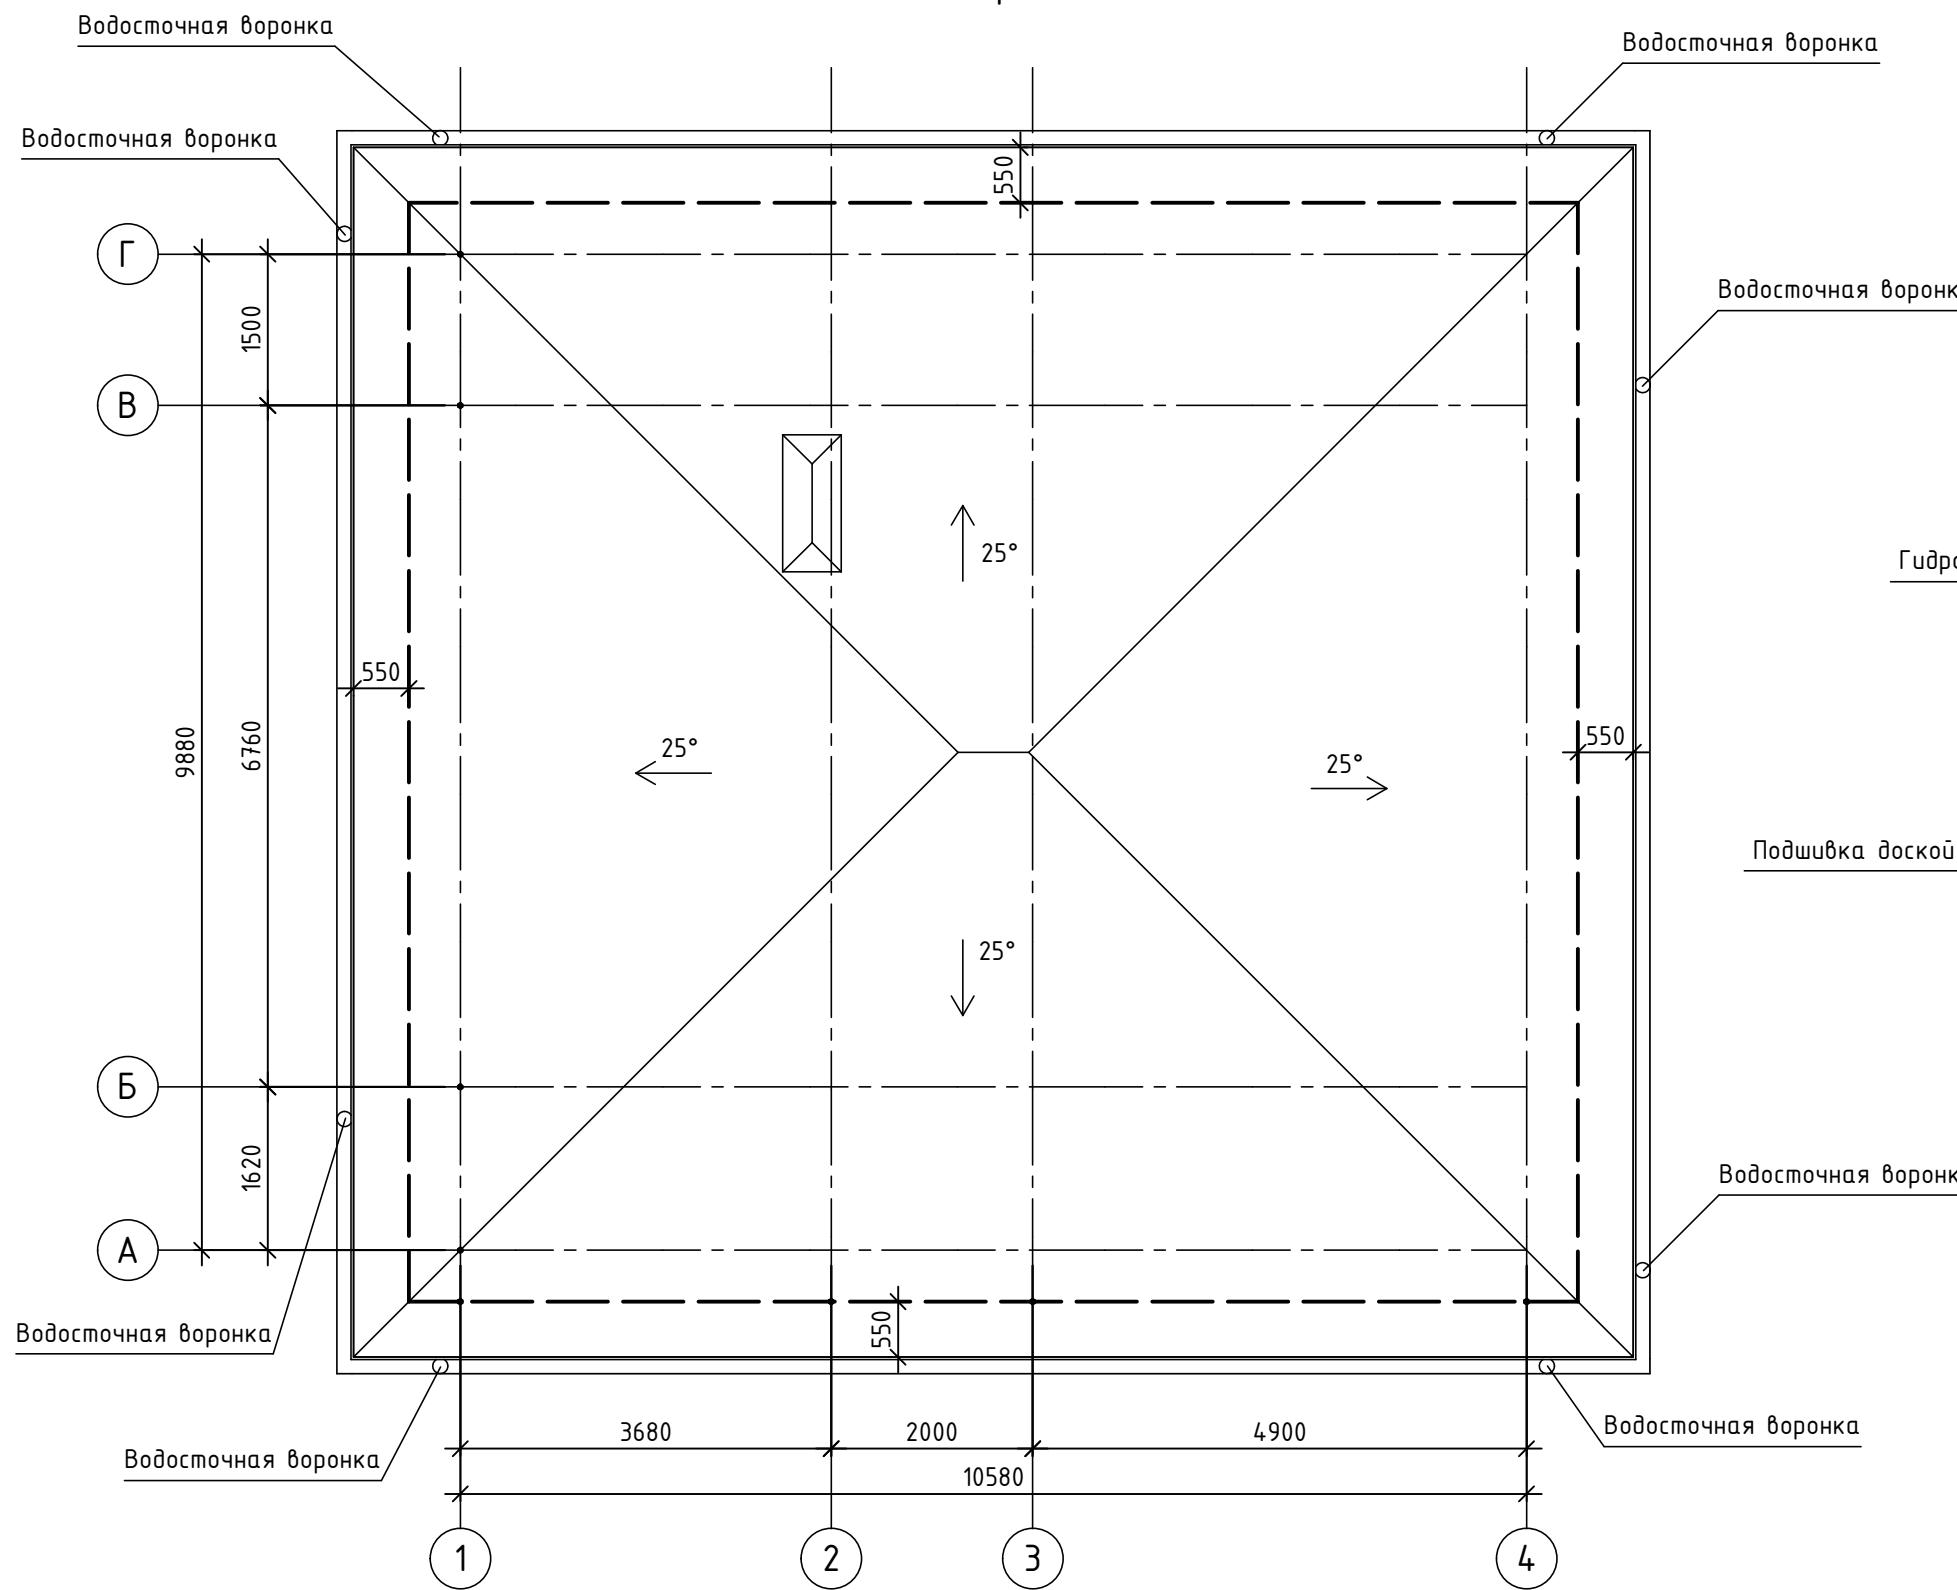


Карнизный узел

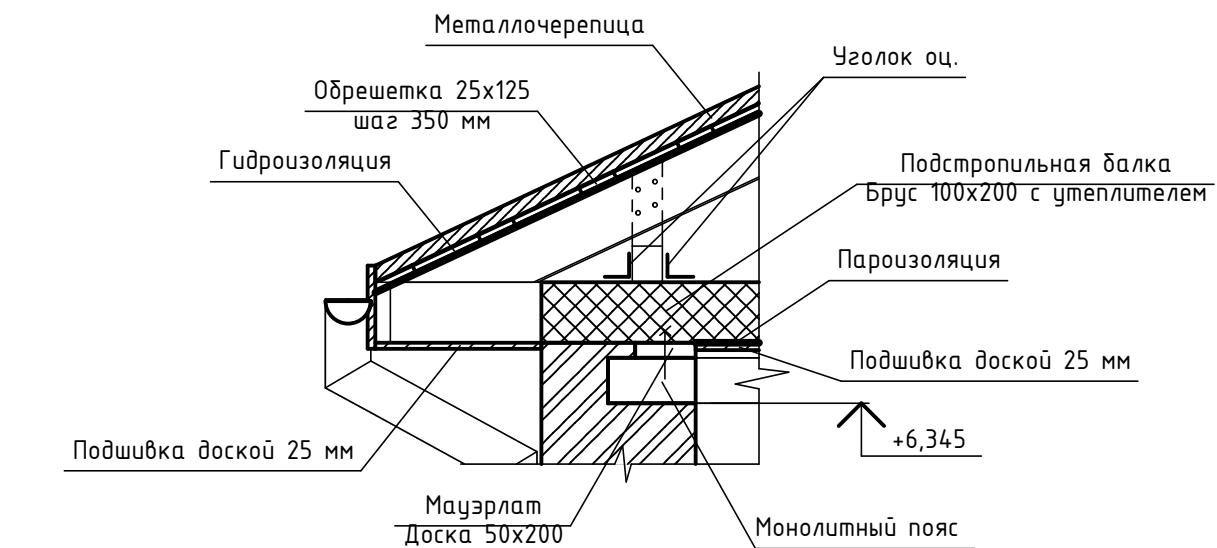

Инф. № подл.	Подпись	Подпись и дата	Взам. инф. №
--------------	---------	----------------	--------------


Изм.	Кол.уч	Лист	№док	Подпись	Дата	АР
Разработ.						Индивидуальный жилой дом
Проверил						Компейдж
						Стадия
						Лист
						Листов
						8
Н.контр.						План кровли

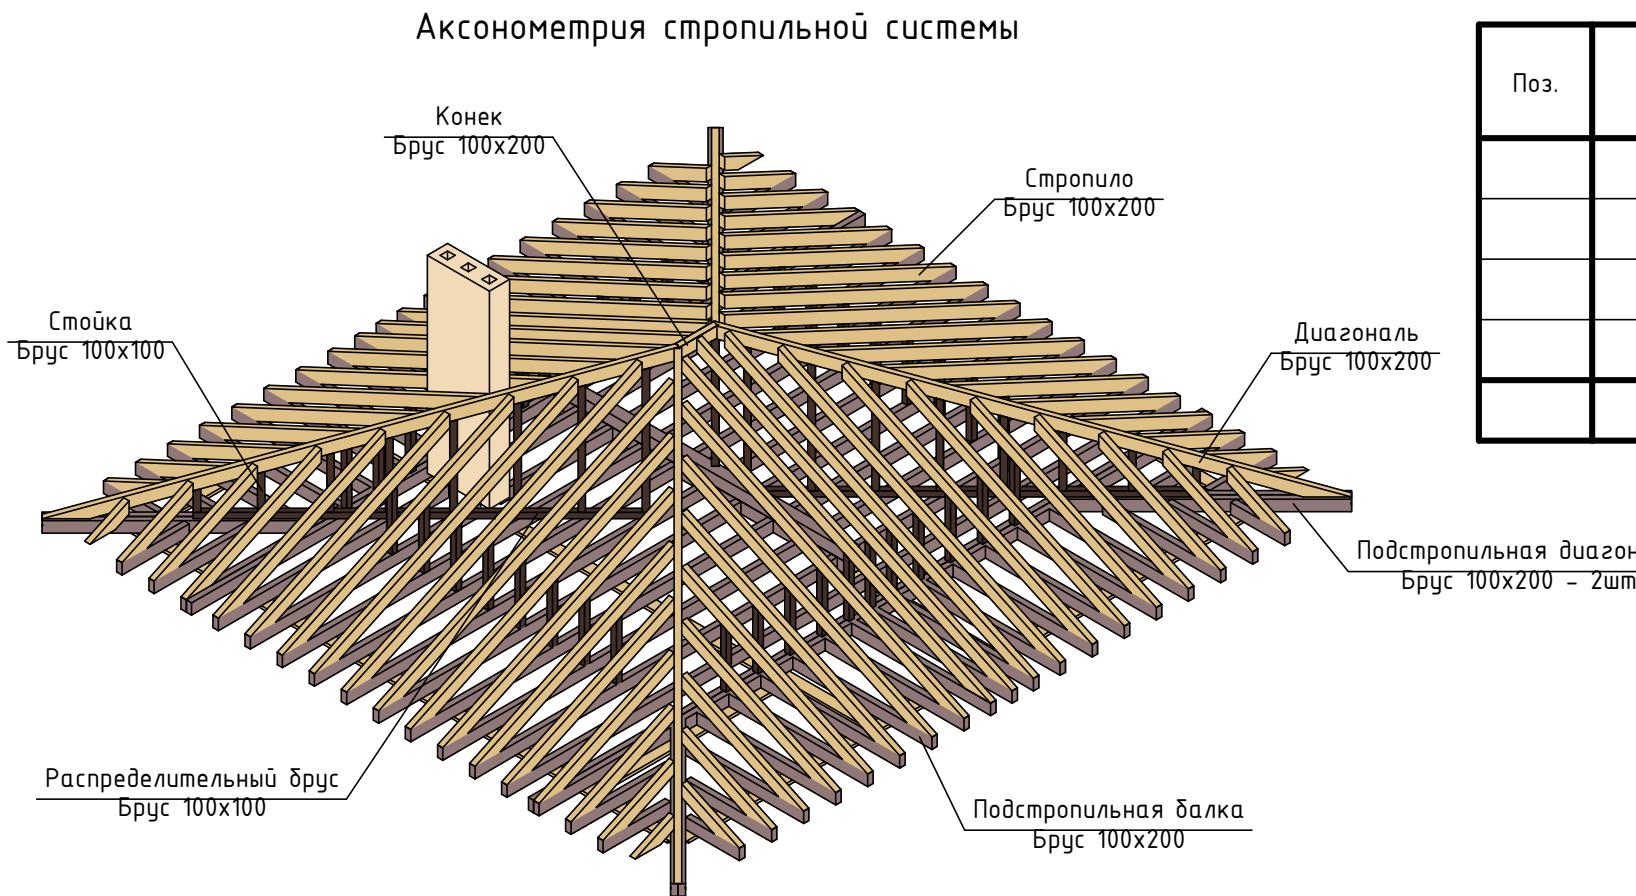

Спецификация элементов стропильной системы

Поз.	Обозначение	Наименование	Кол-во шт	Объем, м ³	Примечание
		Брус 50x200	1	0.62	
		Брус 100x100	1	1.07	
		Брус 100x200	1	11.85	
		Брус 200x200	1	0.48	
	Итого:			14.03	

План стропильной системы

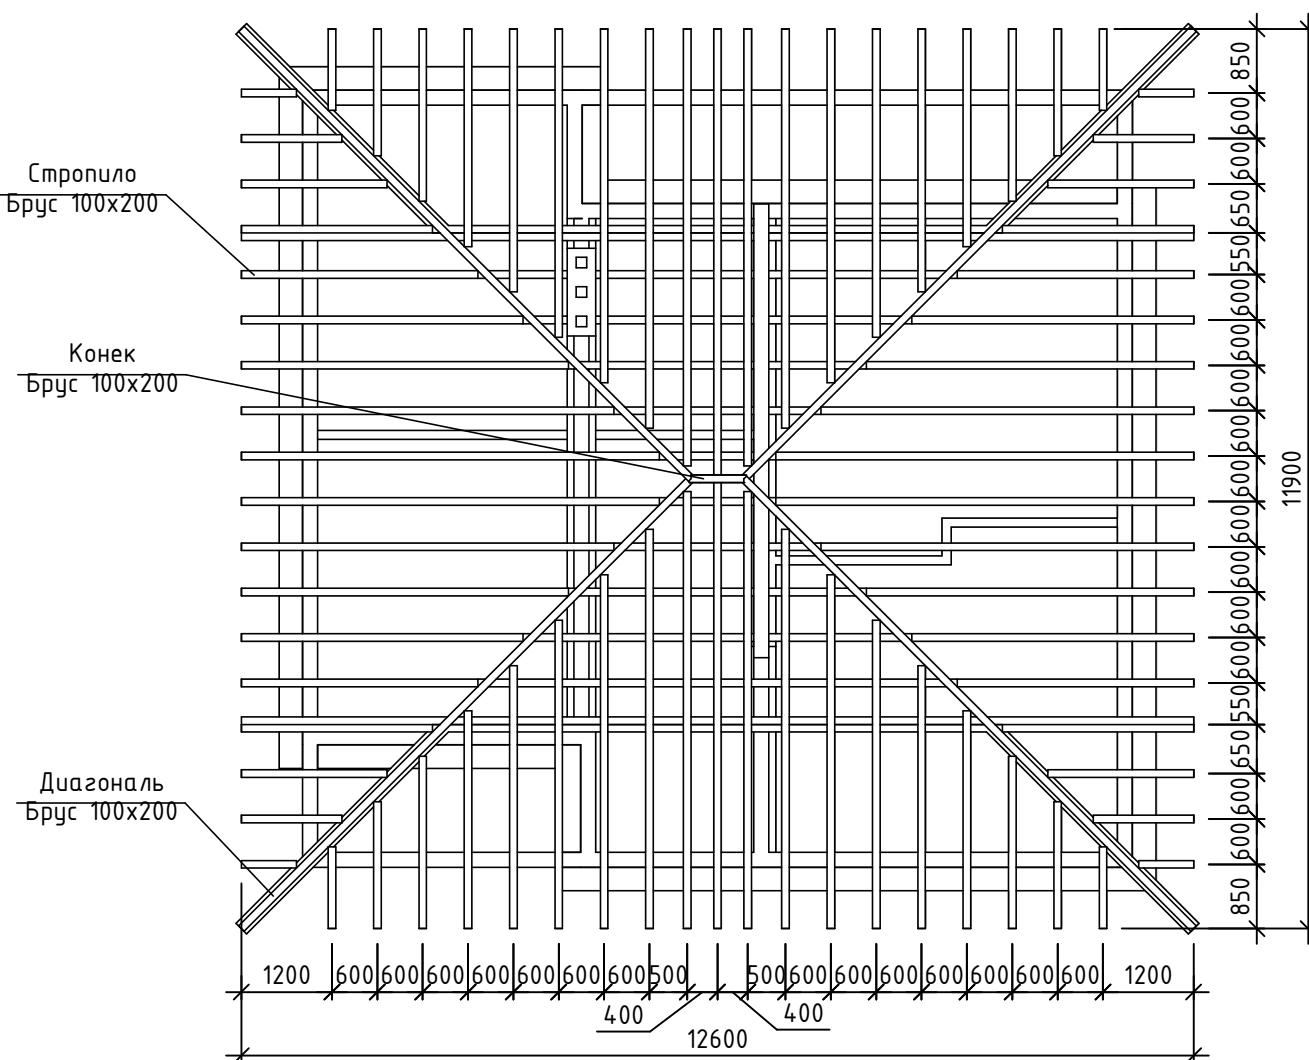

Инв. № подл
Подпись и дата
Взам. инв. №

Изм.	Кол.уч	Лист	№док	Подпись	Дата	AP
Разработ.						Индивидуальный жилой дом
Проверил						Компейдж
Н.контр.						Схема стропильной системы
						Стадия
						Лист
						Листов
						9

Спецификация элементов заполнения дверных проемов

Марка	ГОСТ	Ширина, мм	Высота, мм	Кол-во, шт	Открывание двери
Внутренняя двупольная распашная					
Д1	ГОСТ 6629-88	1 300	2 100	1	Левая
Внутренняя однопольная распашная					
Д2	ГОСТ 6629-88	920	2 100	1	Левая
		920	2 100	1	
		920	2 100	1	
		920	2 100	1	
		920	2 100	1	
		920	2 100	1	
Д3		920	2 100	1	Правая
		920	2 100	1	
Наружная двупольная остекленная					
Д4	ГОСТ 30970-2002	1 650	2 370	1	Левая
		1 650	2 370	1	
		1 650	2 370	1	
Д5		1 300	2 370	1	
Наружная однопольная распашная					
Д6	ГОСТ 30970-2002	800	2 370	1	Левая
	Итого:			13	


Спецификация элементов заполнения оконных проемов

Марка	ГОСТ	Высота, мм	Ширина, мм	Кол-во, шт	Общая площадь м ²
Двустворчатое окно					
OK1	ГОСТ 30674-99	1 600	1 200	1	1.92
OK2	ГОСТ 30674-99	1 600	1 650	2	2.64
Одностворчатое окно					
OK2	ГОСТ 30674-99	1 600	600	1	0.96
OK4	ГОСТ 30674-99	1 600	700	8	1.12
OK5	ГОСТ 30674-99	3 400	700	1	2.38
	Итого:			13	9.02


AP

Индивидуальный жилой дом

Ориентировочная схема расстановки мебели на 1-м этаже

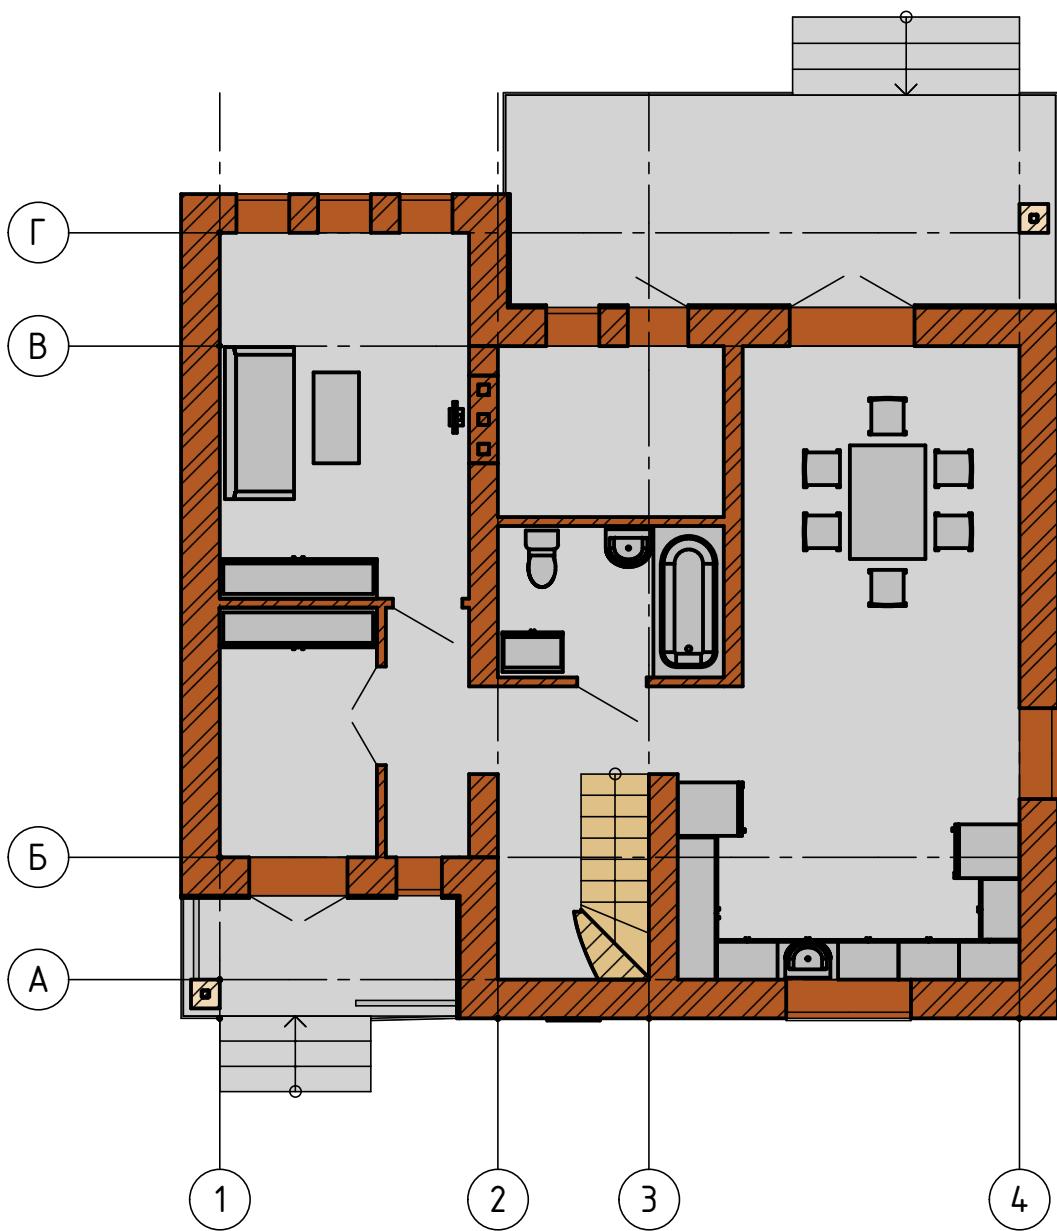

Ориентировочная схема расстановки мебели на 2-м этаже

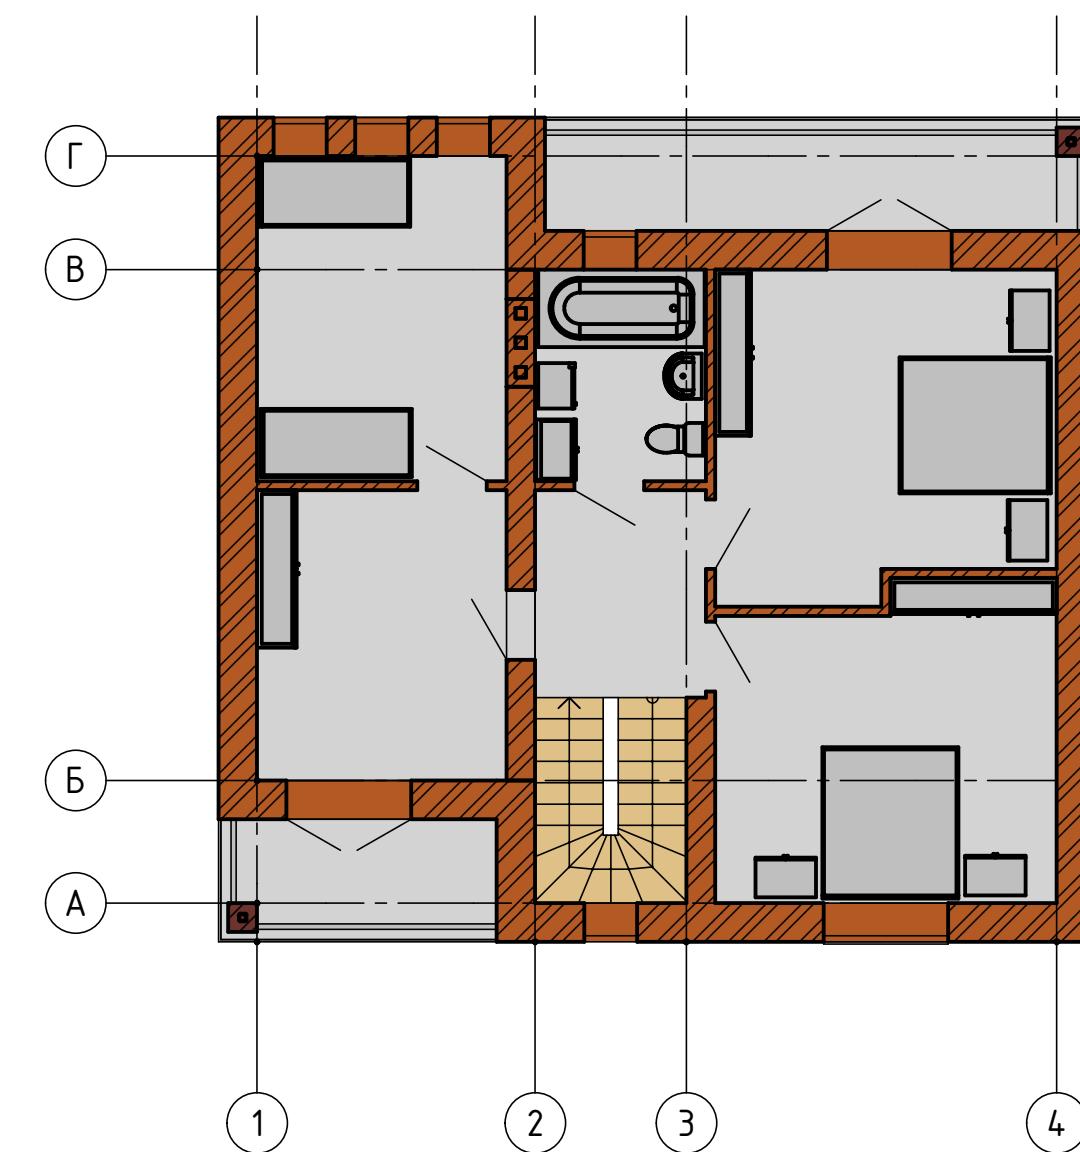

Инв. № подл.	Подпись и дата	Взам. инв. №
--------------	----------------	--------------

Изм.	Кол.уч	Лист	№док	Подпись	Дата	АР
Разработ.						Индивидуальный жилой дом
Проверил						Компейдж
						Стадия
						Лист
						Листов
						11
Н.контр.						Ориентировочная схема расстановки мебели